


Les Veilleurs — La vitrine lenticulaire — Croquis de principe d'origine — coupe dans le montant

LV-VL-CRQ-01 · rév. 1 · 24-09-26 · ESQUISSE · schéma légendé en français

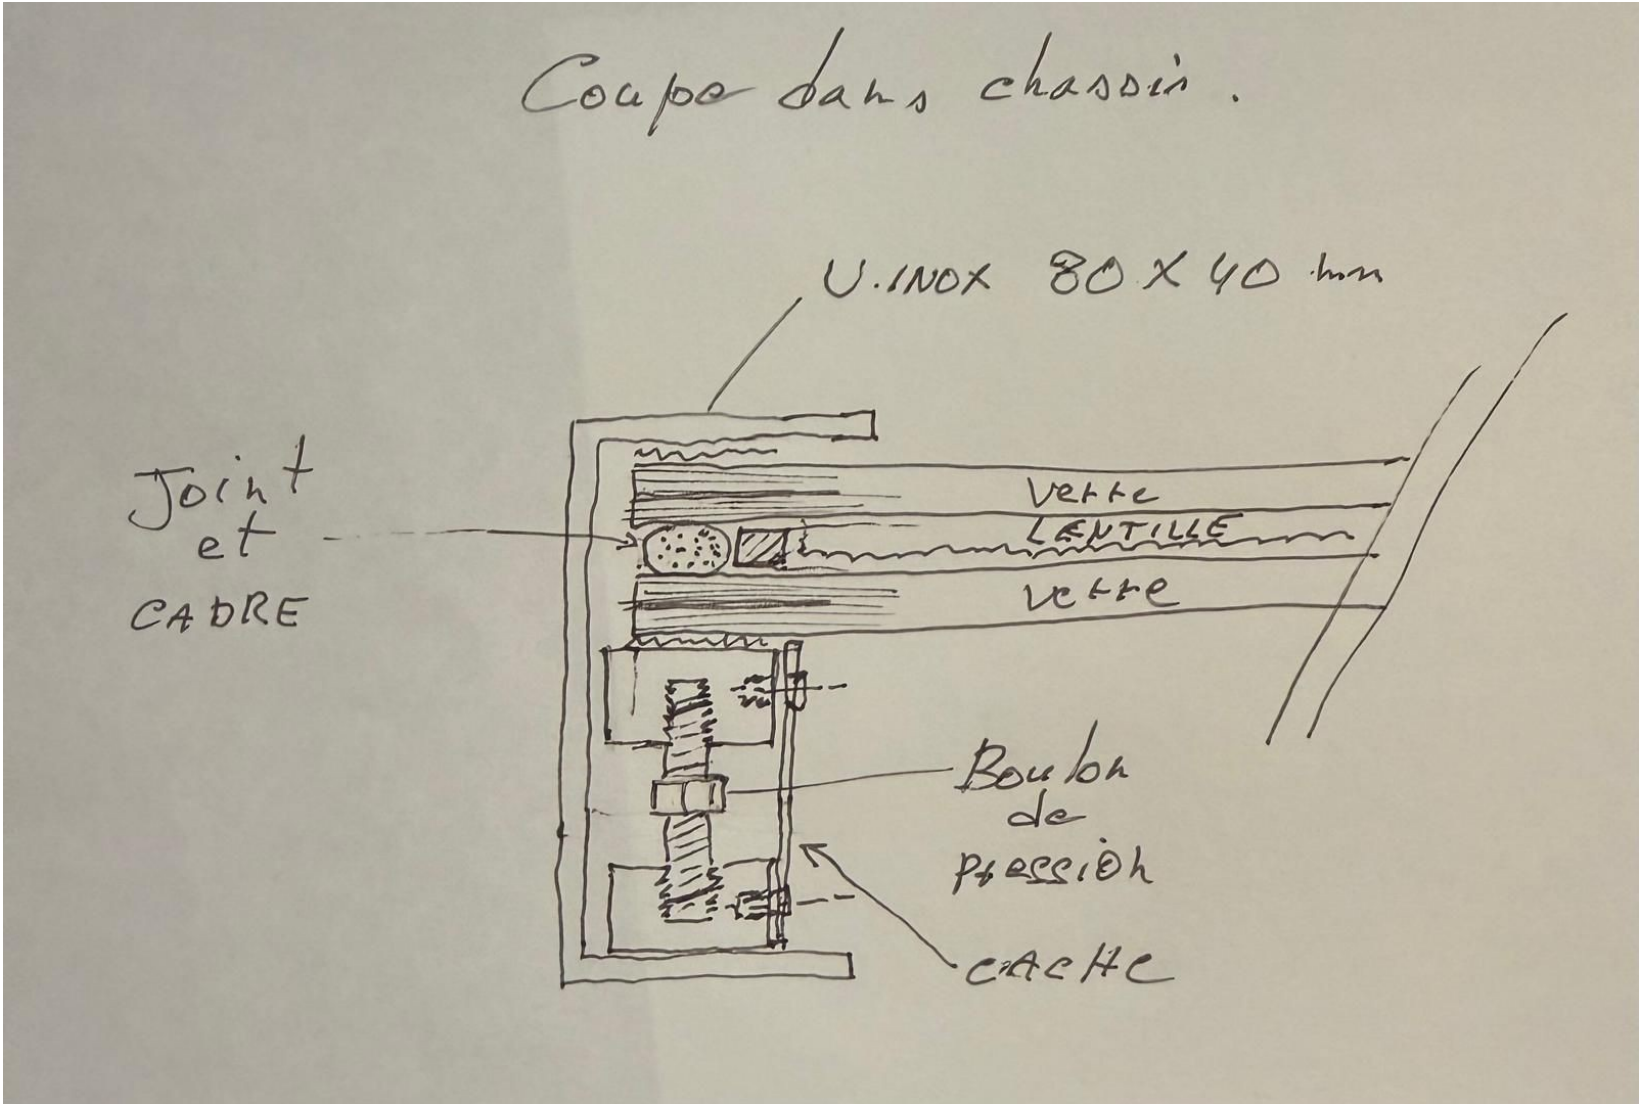

PROJET LES VEILLEURS — Beaufort 27 ARTISTE · MAÎTRE D'ŒUVRE Eva L'Hoest · +32 495 57 92 12 · eva.lhoest@gmail.com ASSISTANT ÉLECTROMÉCANIQUE Gioacchino Miceli · +32 497 84 45 10 · gioacchino.miceli@thefactory.com	DOCUMENT La vitrine lenticulaire — Croquis de principe d'origine — coupe dans le montant OBJET Double vitrage démontable, lenticulaire libre, châssis U inox N° DOCUMENT · RÉVISION · DATE · HEURE LV-VL-CRQ-01 · rév. 1 · 24-09-26 EN LIGNE https://vitrine-lenticulaire.vercel.app	STATUT ESQUISSE © Eva L'Hoest 2026 — Confidentiel. Reproduction, diffusion ou usage hors de cette consultation interdits sans accord écrit de l'artiste. Cotes non contractuelles.
--	--	---