


Les Veilleurs — La vitrine lenticulaire — Coupe horizontale dans un montant

LV-VL-FIG-02 · rév. 1 · 24-09-26 · ESQUISSE · schéma légendé en français

Coupe horizontale dans un montant – principe du serrage périphérique (échelle ≈ 1:1, cotes en mm)

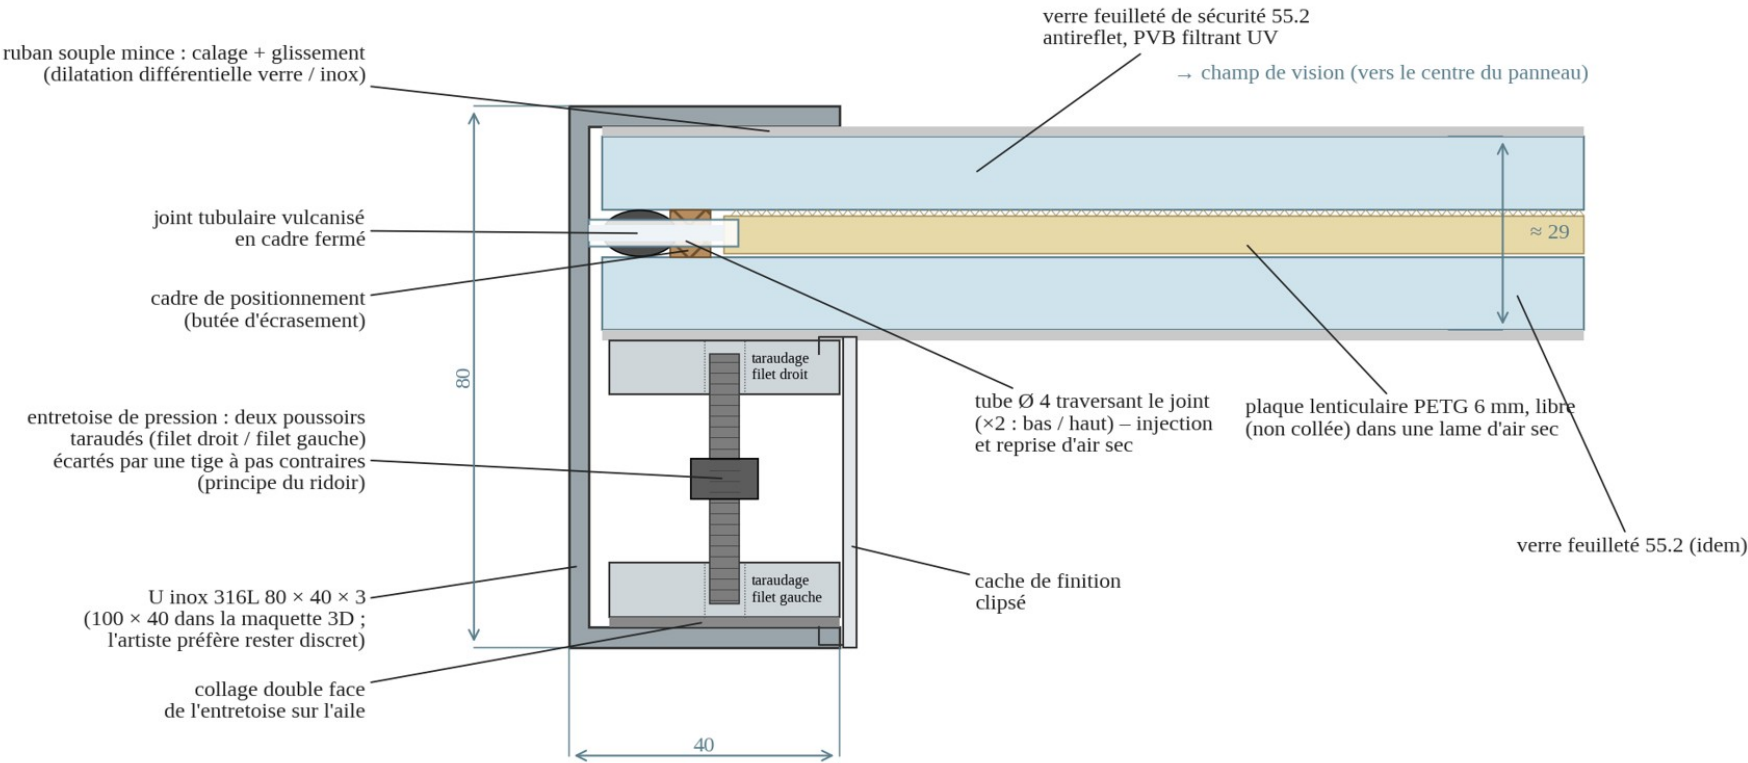

PROJET LES VEILLEURS — Beaufort 27 ARTISTE · MAÎTRE D'ŒUVRE Eva L'Hoest · +32 495 57 92 12 · eva.lhoest@gmail.com ASSISTANT ÉLECTROMÉCANIQUE Gioacchino Miceli · +32 497 84 45 10 · gioacchino.miceli@thefactory.com	DOCUMENT La vitrine lenticulaire — Coupe horizontale dans un montant OBJET Double vitrage démontable, lenticulaire libre, châssis U inox N° DOCUMENT · RÉVISION · DATE · HEURE LV-VL-FIG-02 · rév. 1 · 24-09-26 EN LIGNE https://vitrine-lenticulaire.vercel.app	STATUT ESQUISSE © Eva L'Hoest 2026 — Confidentiel. Reproduction, diffusion ou usage hors de cette consultation interdits sans accord écrit de l'artiste. Cotes non contractuelles.
--	--	---